



CONCEPT, NOT FOR FABRICATION
PRELIMINARY, NOT FOR FABRICATION

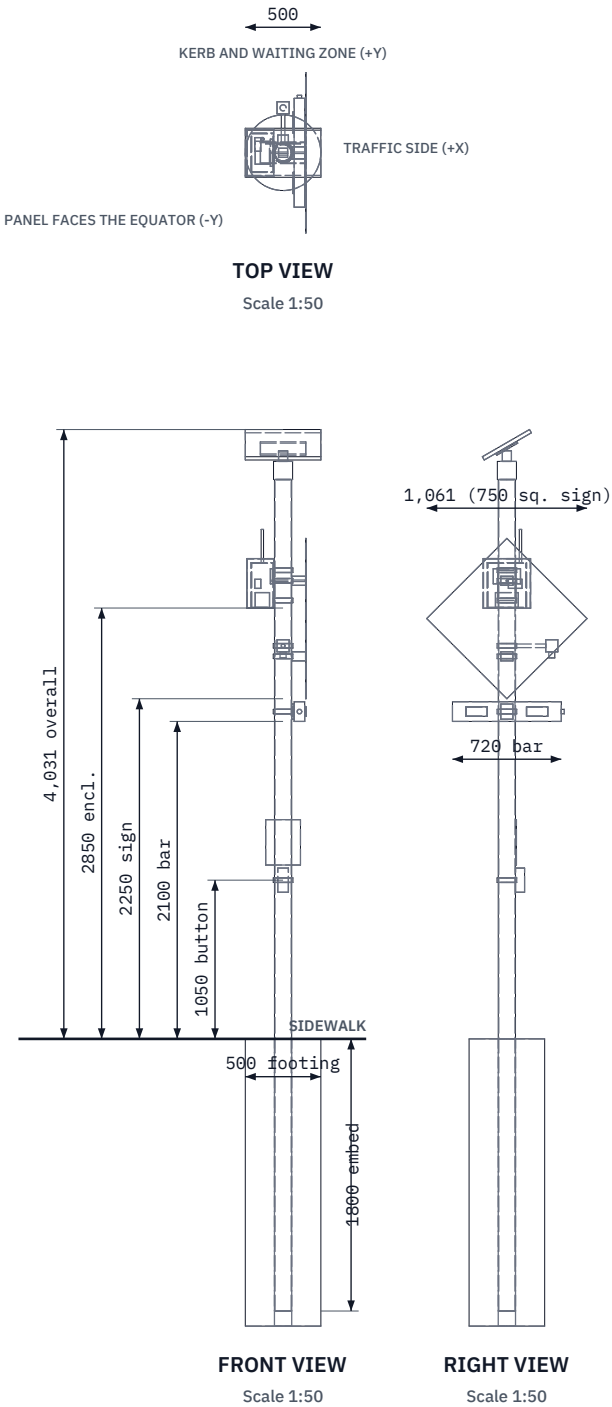

REV	DESCRIPTION	DATE	BY
P1	Preliminary GA for TRL 3 (from cad/src/model.py)	2026-09-25	AC
P2	Sun shield, keyed saddles, anti-rotation bolt (DDR-002)	2026-09-25	AC

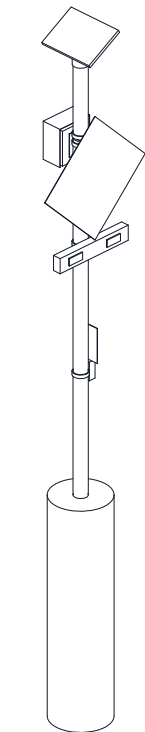

ISOMETRIC VIEW
Not to scale

MAIN DIMENSIONS AND INTERFACES (MM)

Post 114.3 x 3.6 galvanized, 3700 above sidewalk, 1800 in a 500 footing
Existing-pole kit: band clamps for 60 to 114.3 mm poles (no post, no footing)
Sign 750 diamond, 2250 to 3311; faces traffic on +X
Light bar 720 x 70 x 130, bottom 2100; two 140 x 62 heads per face
Pilot light on the kerb end of the bar; button centre 1050
Radar and PIR on a 200 arm at 2600, toward the kerb
Enclosure IP65 150 x 260 x 300, bottom 2850, behind the post
Ventilated sun shield, 25 air gap, roof and three walls, open bottom
Keyed saddles at both sign clamps; new post: M10 through-bolt at the upper saddle
Panel 20 W 500 x 360, tilt 30 deg; top 4,031
Wind case 40 m/s gust: 44 % of S235 yield (CRS-CAL-001 v0.2)
Third-angle; front view from -Y; post on the Z axis

CROSSSAFE

General arrangement, one beacon assembly

DRAWING NO. CRS-DWG-001			REV P2	SHEET 1 of 1	SIZE ANSI B
SCALE 1:50	UNITS mm	PROJECTION 	DATE 2026-09-25		DRAWN Amish Chadha
MATERIAL / NOTES Galvanized steel post; bought-in parts per bom/bom.csv. PRELIMINARY, NOT FOR FABRICATION					
Licensed CERN-OHL-S-2.0 · Design Molecule Lab · designmolecule.com					Generated from cad/src; do not edit by hand