
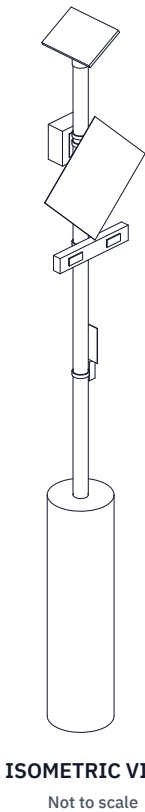
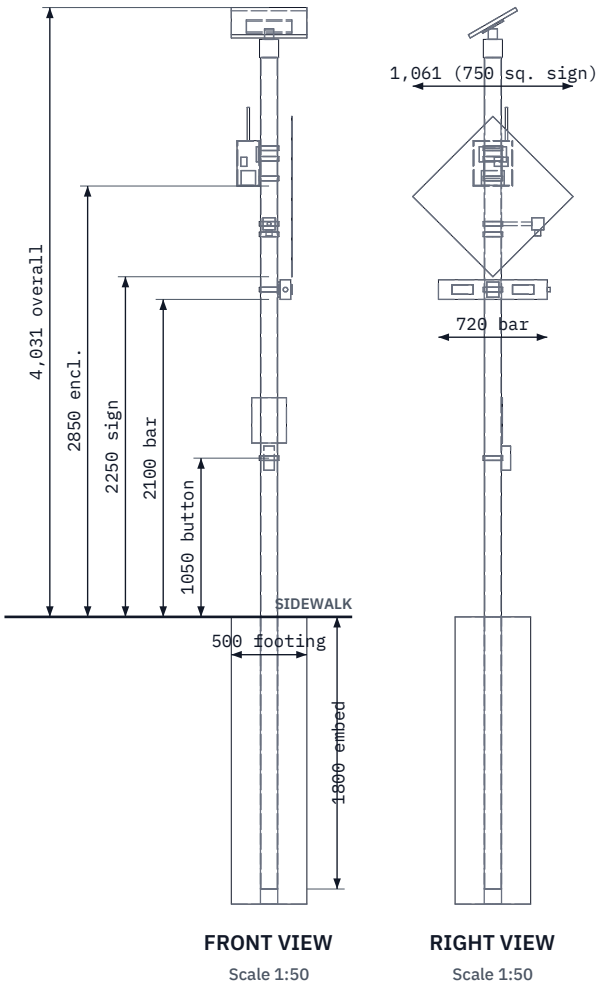


CONCEPT, NOT FOR FABRICATION
PRELIMINARY, NOT FOR FABRICATION

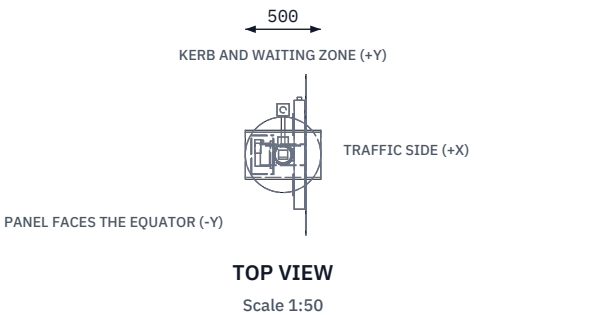

MAIN DIMENSIONS AND INTERFACES (MM)

- Post 114.3 x 3.6 galvanized, 3700 above sidewalk, 1800 in a 500 footing
- Existing-pole kit: band clamps for 60 to 114.3 mm poles (no post, no footing)
- Sign 750 diamond, 2250 to 3311; faces traffic on +X
- Light bar 720 x 70 x 130, bottom 2100; two 140 x 62 heads per face
- Pilot light on the kerb end of the bar; button centre 1050
- Radar and PIR on a 200 arm at 2600, toward the kerb
- Enclosure IP65 150 x 260 x 300, bottom 2850, behind the post
- Panel 20 W 500 x 360, tilt 30 deg; top 4,031
- Wind case 40 m/s gust: 42 % of S235 yield (CRS-CAL-001)
- Third-angle; front view from -Y; post on the Z axis

CROSSSAFE

General arrangement, one beacon assembly

DRAWING NO. CRS-DWG-001			REV P1	SHEET 1 of 1	SIZE ANSI B
SCALE 1:50	UNITS mm	PROJECTION 	DATE 2026-09-25		DRAWN Amish Chadha
MATERIAL / NOTES Galvanized steel post; bought-in parts per bom/bom.csv. PRELIMINARY, NOT FOR FABRICATION					
Licensed CERN-OHL-S-2.0 · Open Hardware Portfolio · amishchadha.com				Generated from cad/src; do not edit by hand	